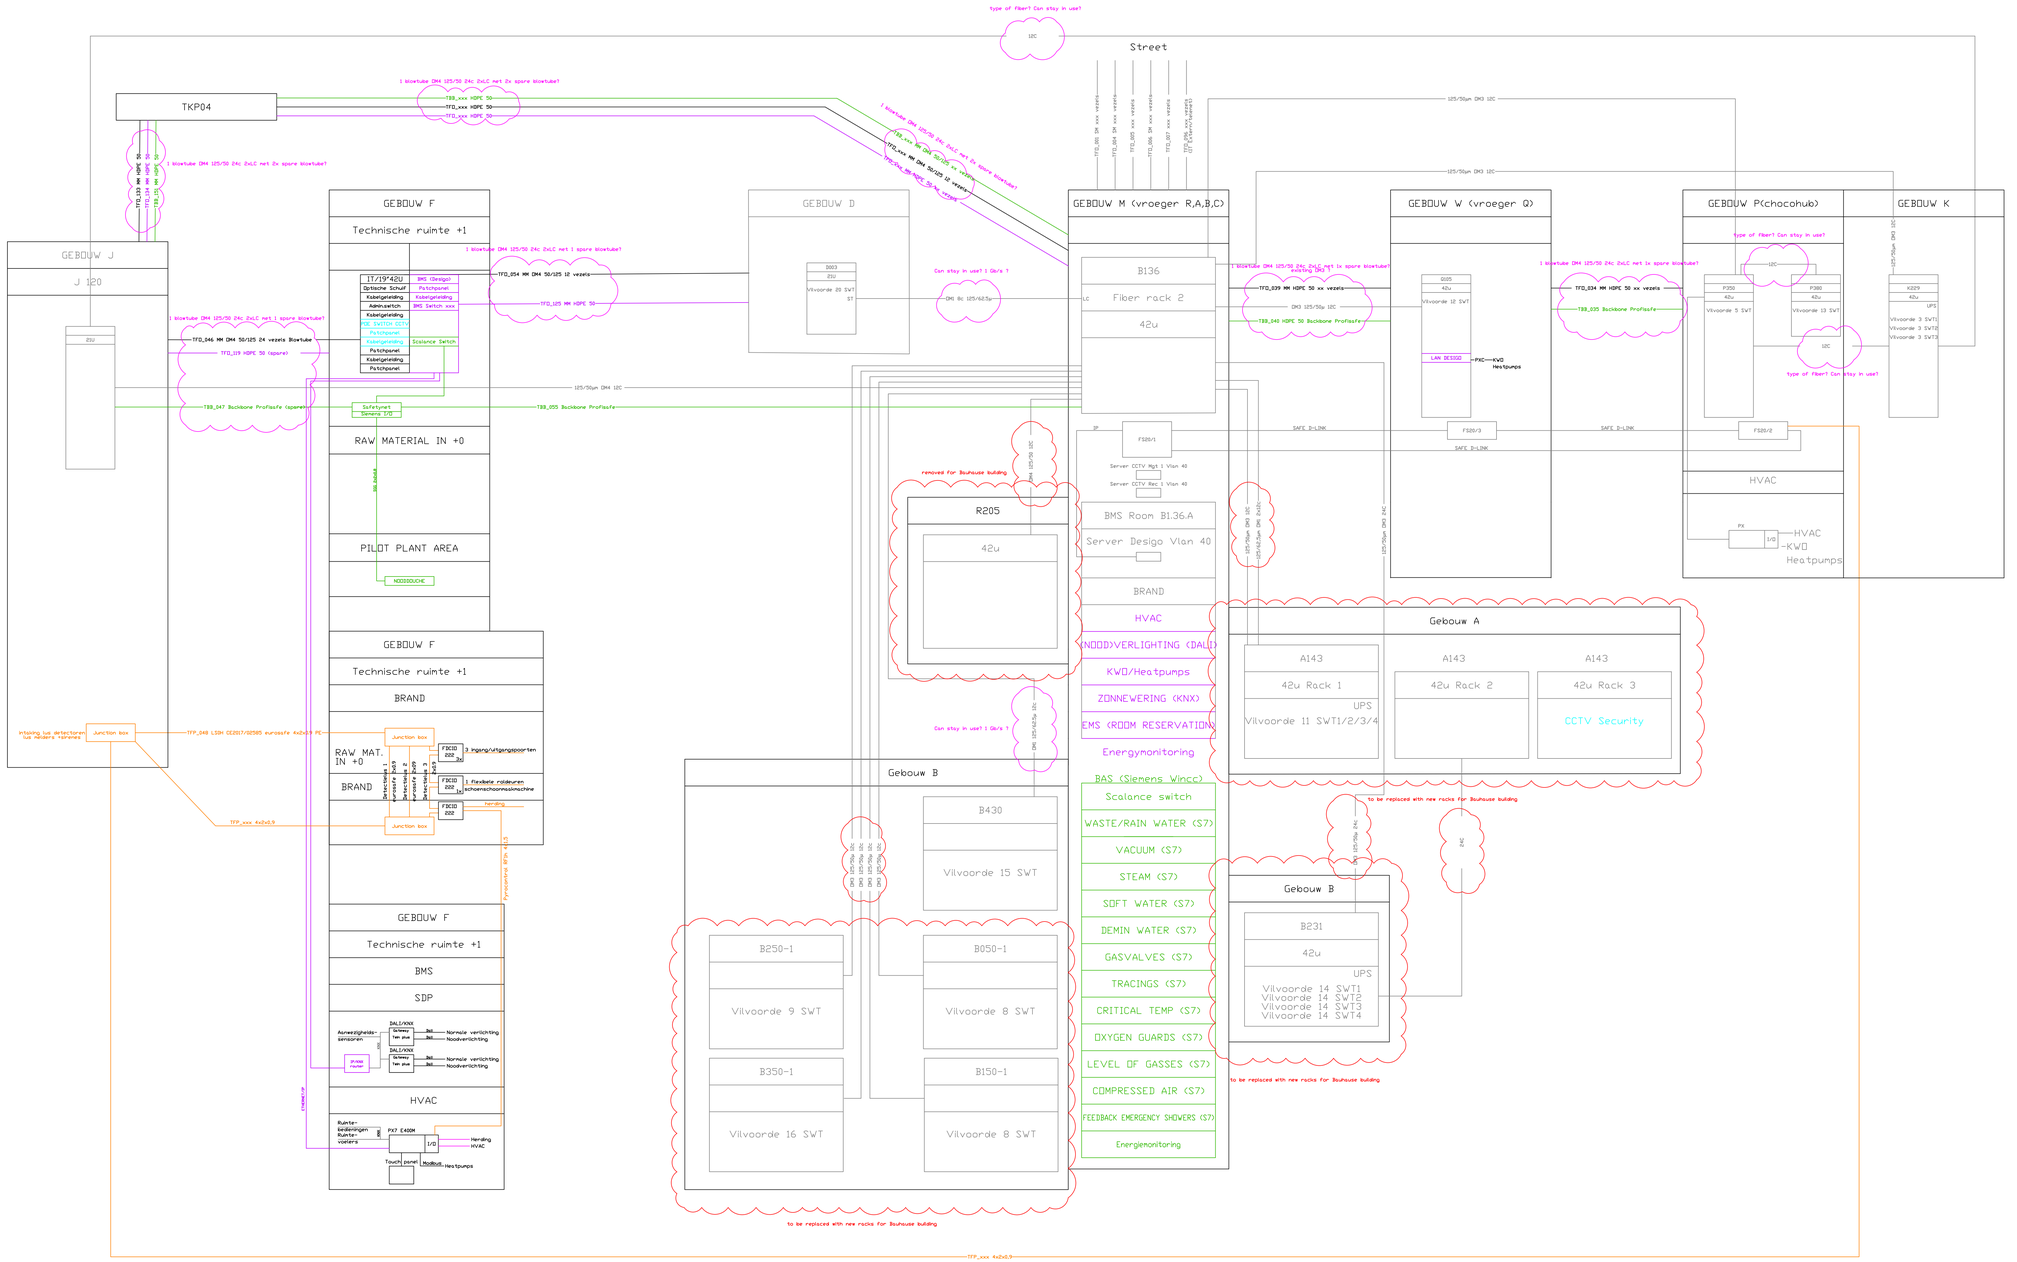


NEW Networks

- FIRE
- LAN Building Management system (Desigo)
- LAN BAS (S7/Siemens Wincc)
- LAN Administrative (IT)
- CCTV (POE)

Existing networks

- Cabinets/FO

To be demolished

- Cabinets/FO

REV.	DATUM	DOOR	OMSCHRIJVING	Naam CONTROLE	Par. CONTROLE	Naam AUTORISATIE	Par. AUTORISATIE
4	05/06/'25	FrBu	modified after IT meeting 5/06				
3	15/05/'25	FrBu	Input meeting 12/05/'25 added				
2	05/'25	FrBu	Draft				
1	07/05/'24	FrBu	Eerste uitgave				

Opdrachtgever	: Cargill
Project	: F-Gebouw
Onderwerp	: Network Diagram
Klant doc. nr.:	
Schaal	:
Formaat	: A
Rev. :	4
Doc. nr. :	60510015-EL-DW-0002

Sweco Belgium nv
Division Industry